PROPOSAL-01

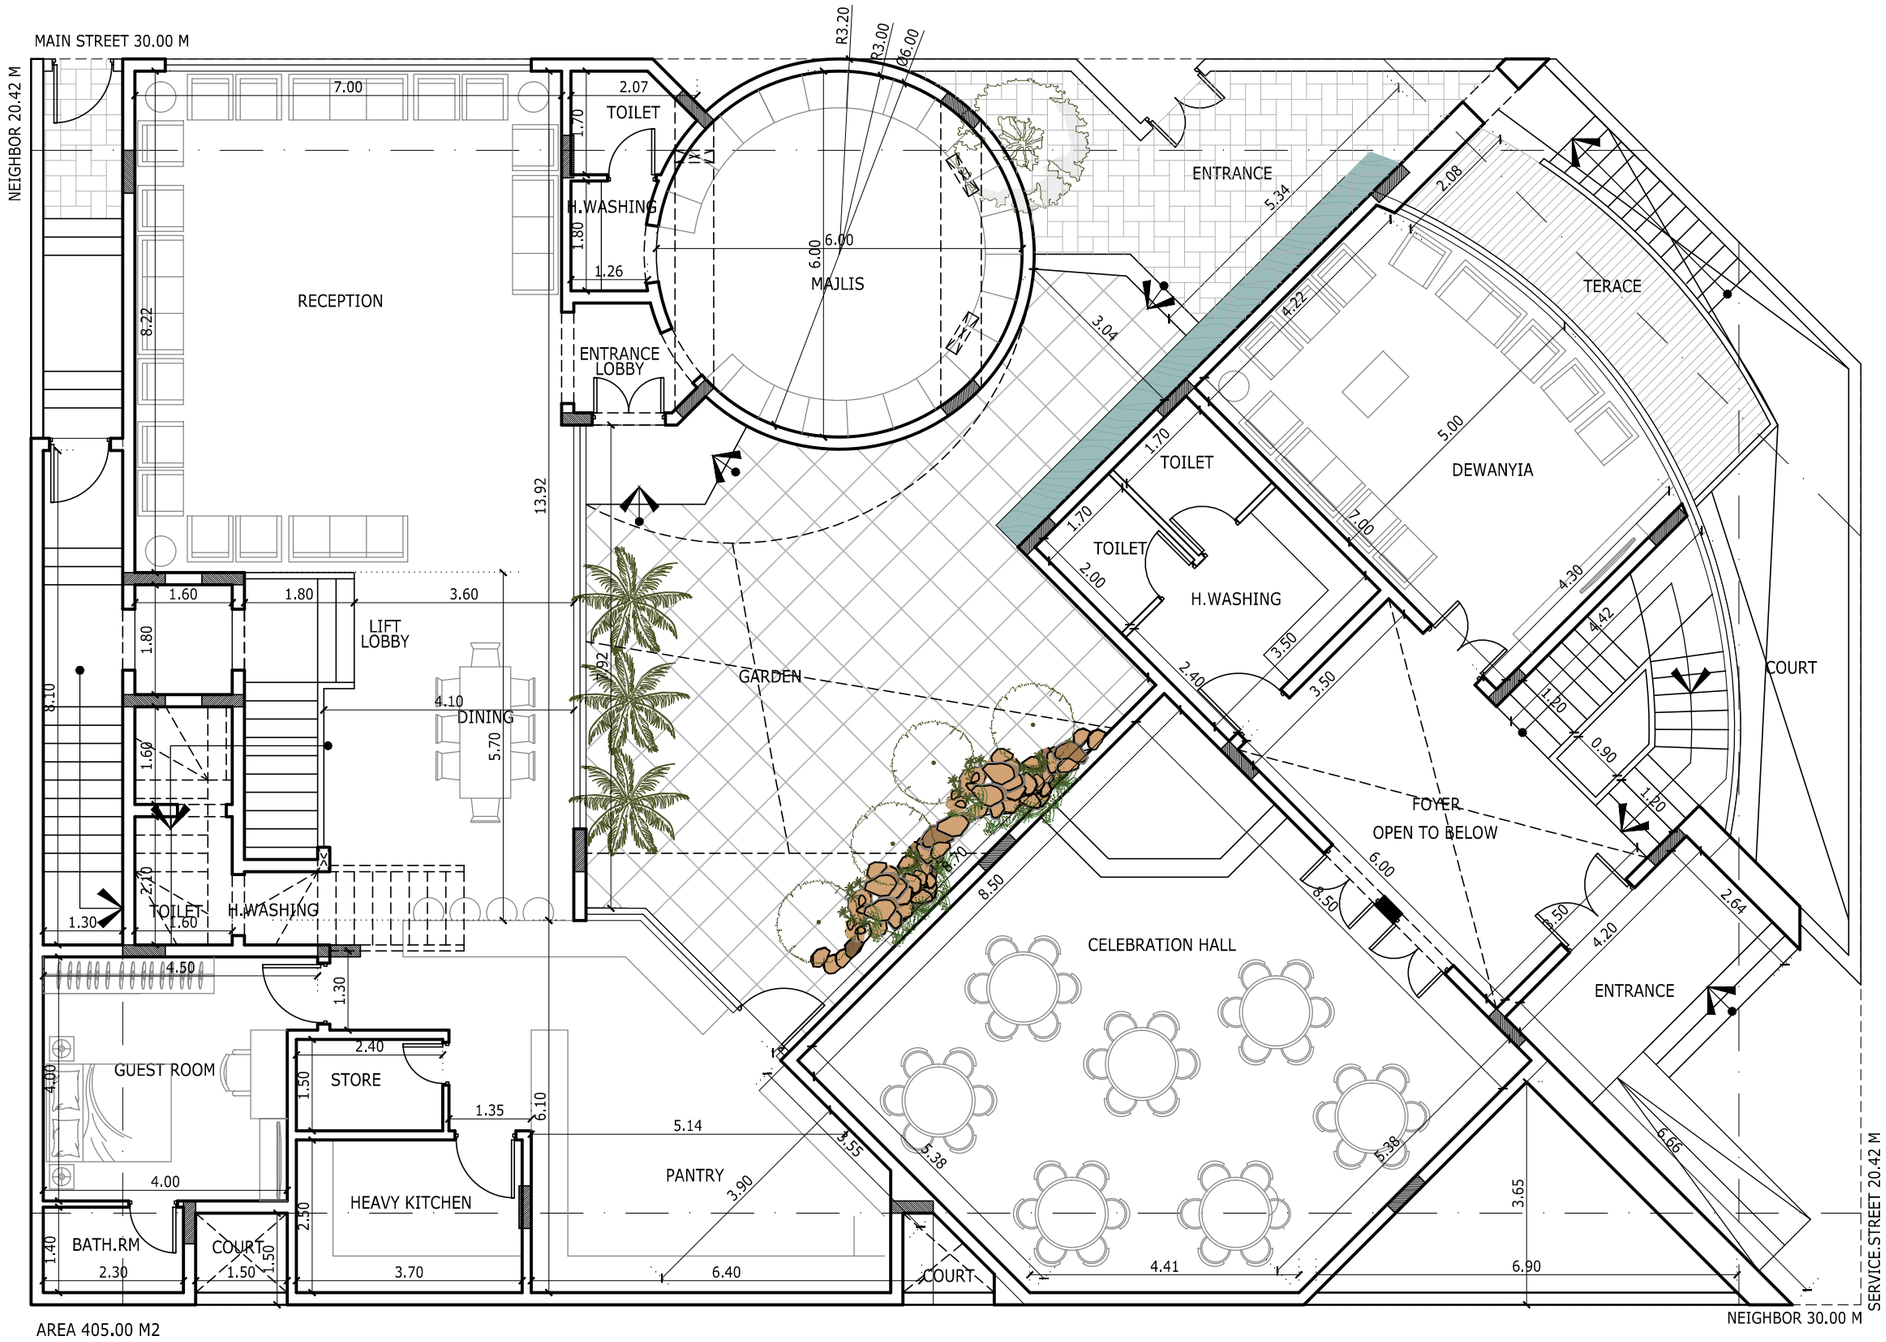

AREA 405.00 M2

SHEET A2 (420X297)

C:\Users\Cristina\AppData\Local\Microsoft\Windows\Temporary Internet Files\Content.Outlook\A9L1RX2S\2015-03-31.dwg

REMARKS:

- ALL DIMENSIONS AND LEVELS ARE METRIC IN (M)
- FFL = FINISHED FLOOR LEVEL
- TOS = TOP OF SLAB
- TOP = TOP OF PARAPET

NOTES :

- ALL DIMENSIONS TO BE VERIFIED ON SITE AND APPROVED BY THE ENGINEER
- THIS DRAWING SHOULD BE READ IN CONJUNCTION WITH OTHER RELEVANT ARCHITECTURAL, STRUCTURAL, MECHANICAL, ELECTRICAL AND SPECIAL SYSTEMS DRAWINGS AND ALL RELEVANT SECTIONS OF THE SPECIFICATIONS
- CONTRACTOR TO CHECK AND COORDINATE ALL ARCHITECTURAL, STRUCTURAL, ELECTROMECHANICAL AND LANDSCAPE WORKS BEFORE CONSTRUCTION
- ALL PILASTERS ARE 130 OR 260MM THK, UNLESS OTHERWISE INDICATED AS SHOWN ON DRAWINGS.
- ALL WALLS ARE 100, 150 ,200 OR 300MM THK, UNLESS OTHERWISE INDICATED AS SHOWN ON DRAWINGS.

KEY PLAN

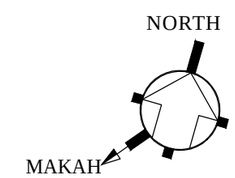

PROJECT NAME:

PRIVATE VILLA

CLIENT:

MR\ Sultan Al-Sbaa'i

DESIGNER & MAIN CONSULTANT:

E / SAMI - E / AHMED SHALTOT
Inverse Consultant
Innovative Designs
PLOT (28A) AL-SOOR ST (2) BLOCK (3)
AL-BAIT AL-ABIED BUILDING
AL-DASMAN, SHARQ, KUWAIT
TEL. +965 22418152
FAX. +965 22418153
Website : www.INVERSE-KW.com
E-mail : INFO INVERSE-KW.com

DRAWING TITLE

GROUND FLOOR LEVEL

DATE	DRAWING BY:	FILE NAME
DEC 2013	MUHMMAD MAGDY	2015-03-31
PROJECT NO.	APPROVED BY:	SCALE
----	AHMED SHALTOOT	NTS
DESIGNED BY:	SHEET:	REV:
MUHMMAD MAGDY MUHMMAD	01	01